

# **OFFALY COUNTY COUNCIL**

## APPENDIX C

### TULLAMORE CYCLE NETWORK PHASE 1

#### DRAWINGS

Tullamore Municipal District,  
Offaly County Council,  
Town Hall,  
Cormac Street,  
Tullamore,  
Co. Offaly.  
Tel: (057)9354270  
Email: [tullamoremd@offalycoco.ie](mailto:tullamoremd@offalycoco.ie)

Tom Shanahan  
Director of Services,  
Offaly County Council,  
Aras an Chontae,  
Charleville Road,  
Tullamore,  
Co. Offaly.


DRAWING NO:            TITLE:

TCN1-20 001	SITE LOCATION MAP
TCN1-20 002	ARDEN VIEW
TCN1-20 003	ARDEN ROAD
TCN1-20 004	COLLINS LANE
TCN1-20 005	CLARA ROAD
TCN1-20 006	COLLINS LANE/EDUCATE TOGETHER
TCN1-20 007	CYCLE LANE CONSTRUCTION DETAIL

SANCTIONING AUTHORITY	DTTAS
SPONSORING TITLE	OFFALY COUNTY COUNCIL - TULLAMORE MUNICIPAL DISTRICT
PROJECT TITLE	TULLAMORE CYCLE NETWORK PHASE 1
DOCUMENT TITLE	APPENDIX 3 - DRAWINGS
FILE	V:\1.0 - FOLDER SET UP NEW\4.0 PROJECTS\4.1 - LIVE PROJECTS\4.1.10 - CYCLE LANES\TULLAMORE CYCLE LANES 2020


Date	Revision	Prepared By	Checked By	Approved By
2020	0	T.R.	J.C.	T.S.

OFFALY COUNTY COUNCIL  
TULLAMORE CYCLE NETWORK PHASE 1  
SITE LOCATION MAP/KEY MAP

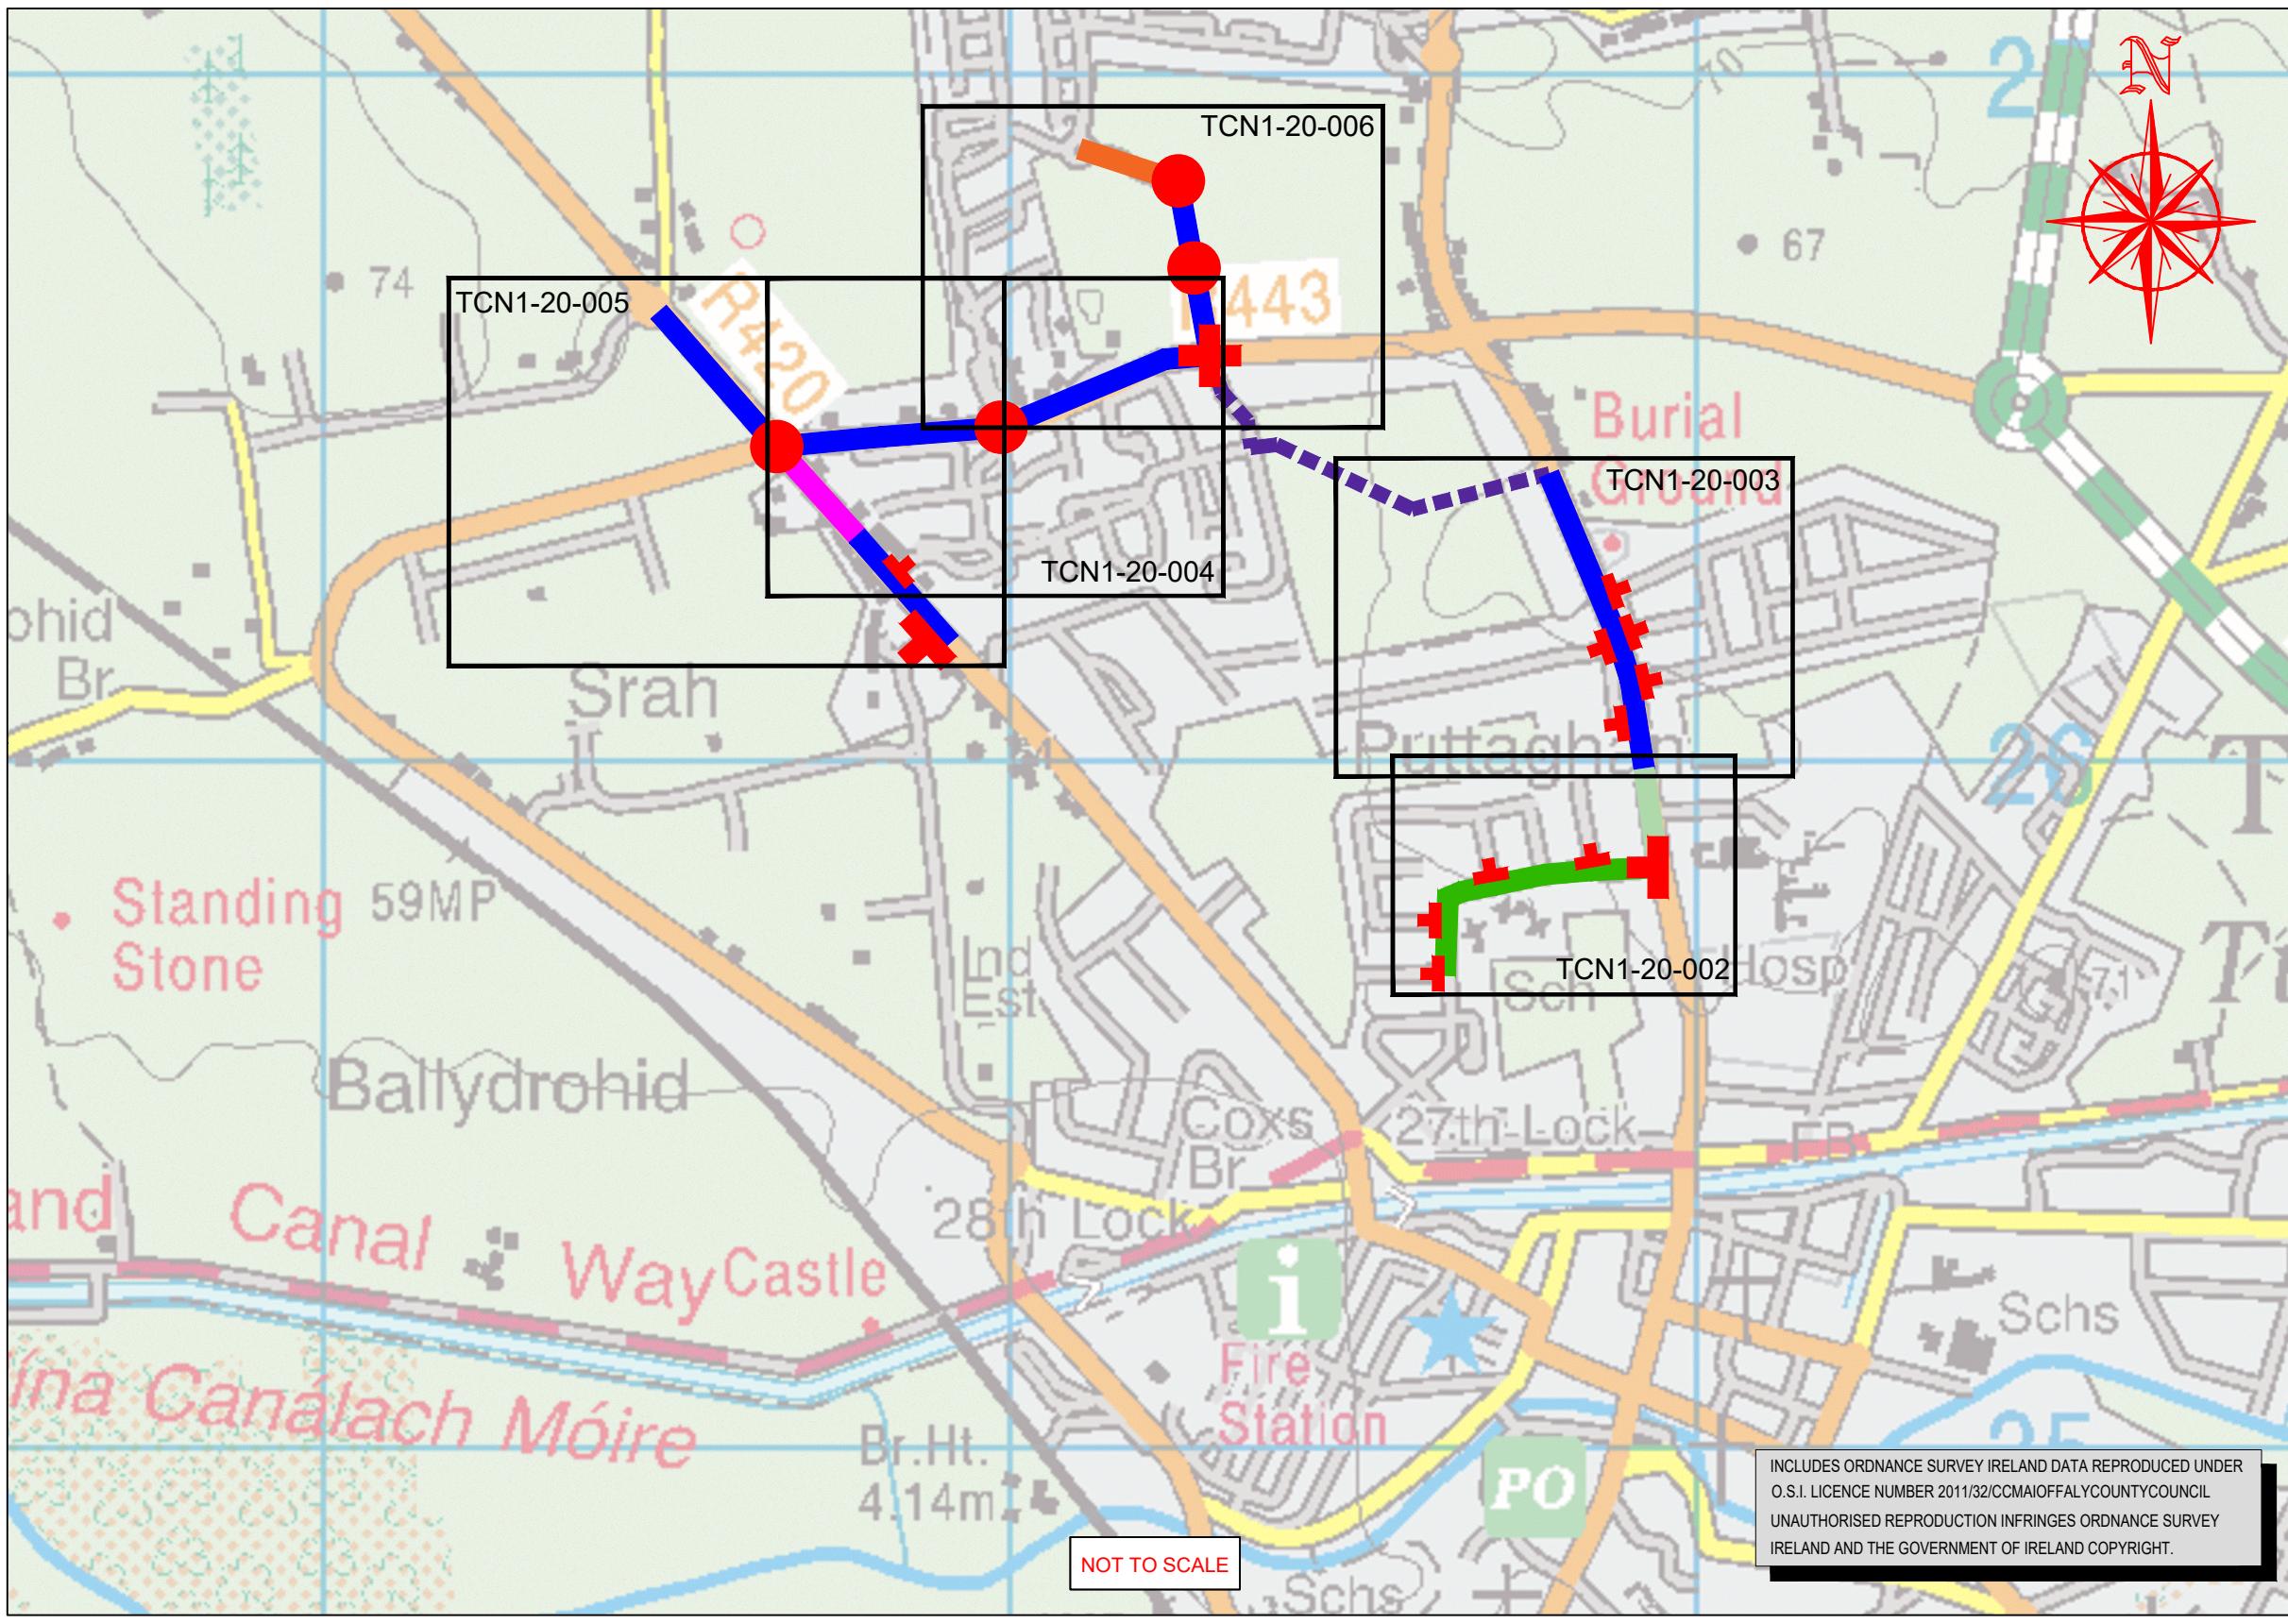

<b>TYPE A</b>		1.8m Path	
		2m Cycle Lane	
		6/6.5m Road	
		2m Cycle Lane 1.8m Path	
<b>TYPE B</b>		3m Shared Surface	
		6/6.5m Road	
		3m Shared Surface	
<b>TYPE C</b>		1.8m Path	
		2m Cycle Verge	
		2m Cycle Lane	
		1m Grass Verge	
		Existing Road	
		1m Grass Verge 1.8m Path	
<b>TYPE D</b>		1.8m Path	
		8.7m Road	
		4m Shared Surface	
<b>TYPE E</b>		1.8m Path	
		2m Cycle Lane	
		2m Cycle Lane	
		Existing Road	
		2m Cycle Lane 1.8m Path	
●	ROUNDABOUT UPGRADE		
+	X-JUNCTION UPGRADE		
+	T-JUNCTION UPGRADE		
LINK THROUGH DEVELOPMENT BY OTHERS			
<b>PRELIMINARY ISSUE</b>			
Tom Shanahan, Director of Services Aras an Chontae, Charleville Rd., Tullamore.			
PROJECT TULLAMORE CYCLE NETWORK PHASE 1			
TITLE SITE LOCATION MAP/KEY MAP			
SCALE AS SHOWN	ROAD NO N/A	PROJECT NO TCN1	DRAWING NO 20 001
	DATE SEPT 2020	DRAWN BY T.R.	CHECKED J.C.

OFFALY COUNTY COUNCIL  
TULLAMORE CYCLE NETWORK PHASE 1  
PROPOSED ARDEN VIEW/ARDEN ROAD LAYOUT

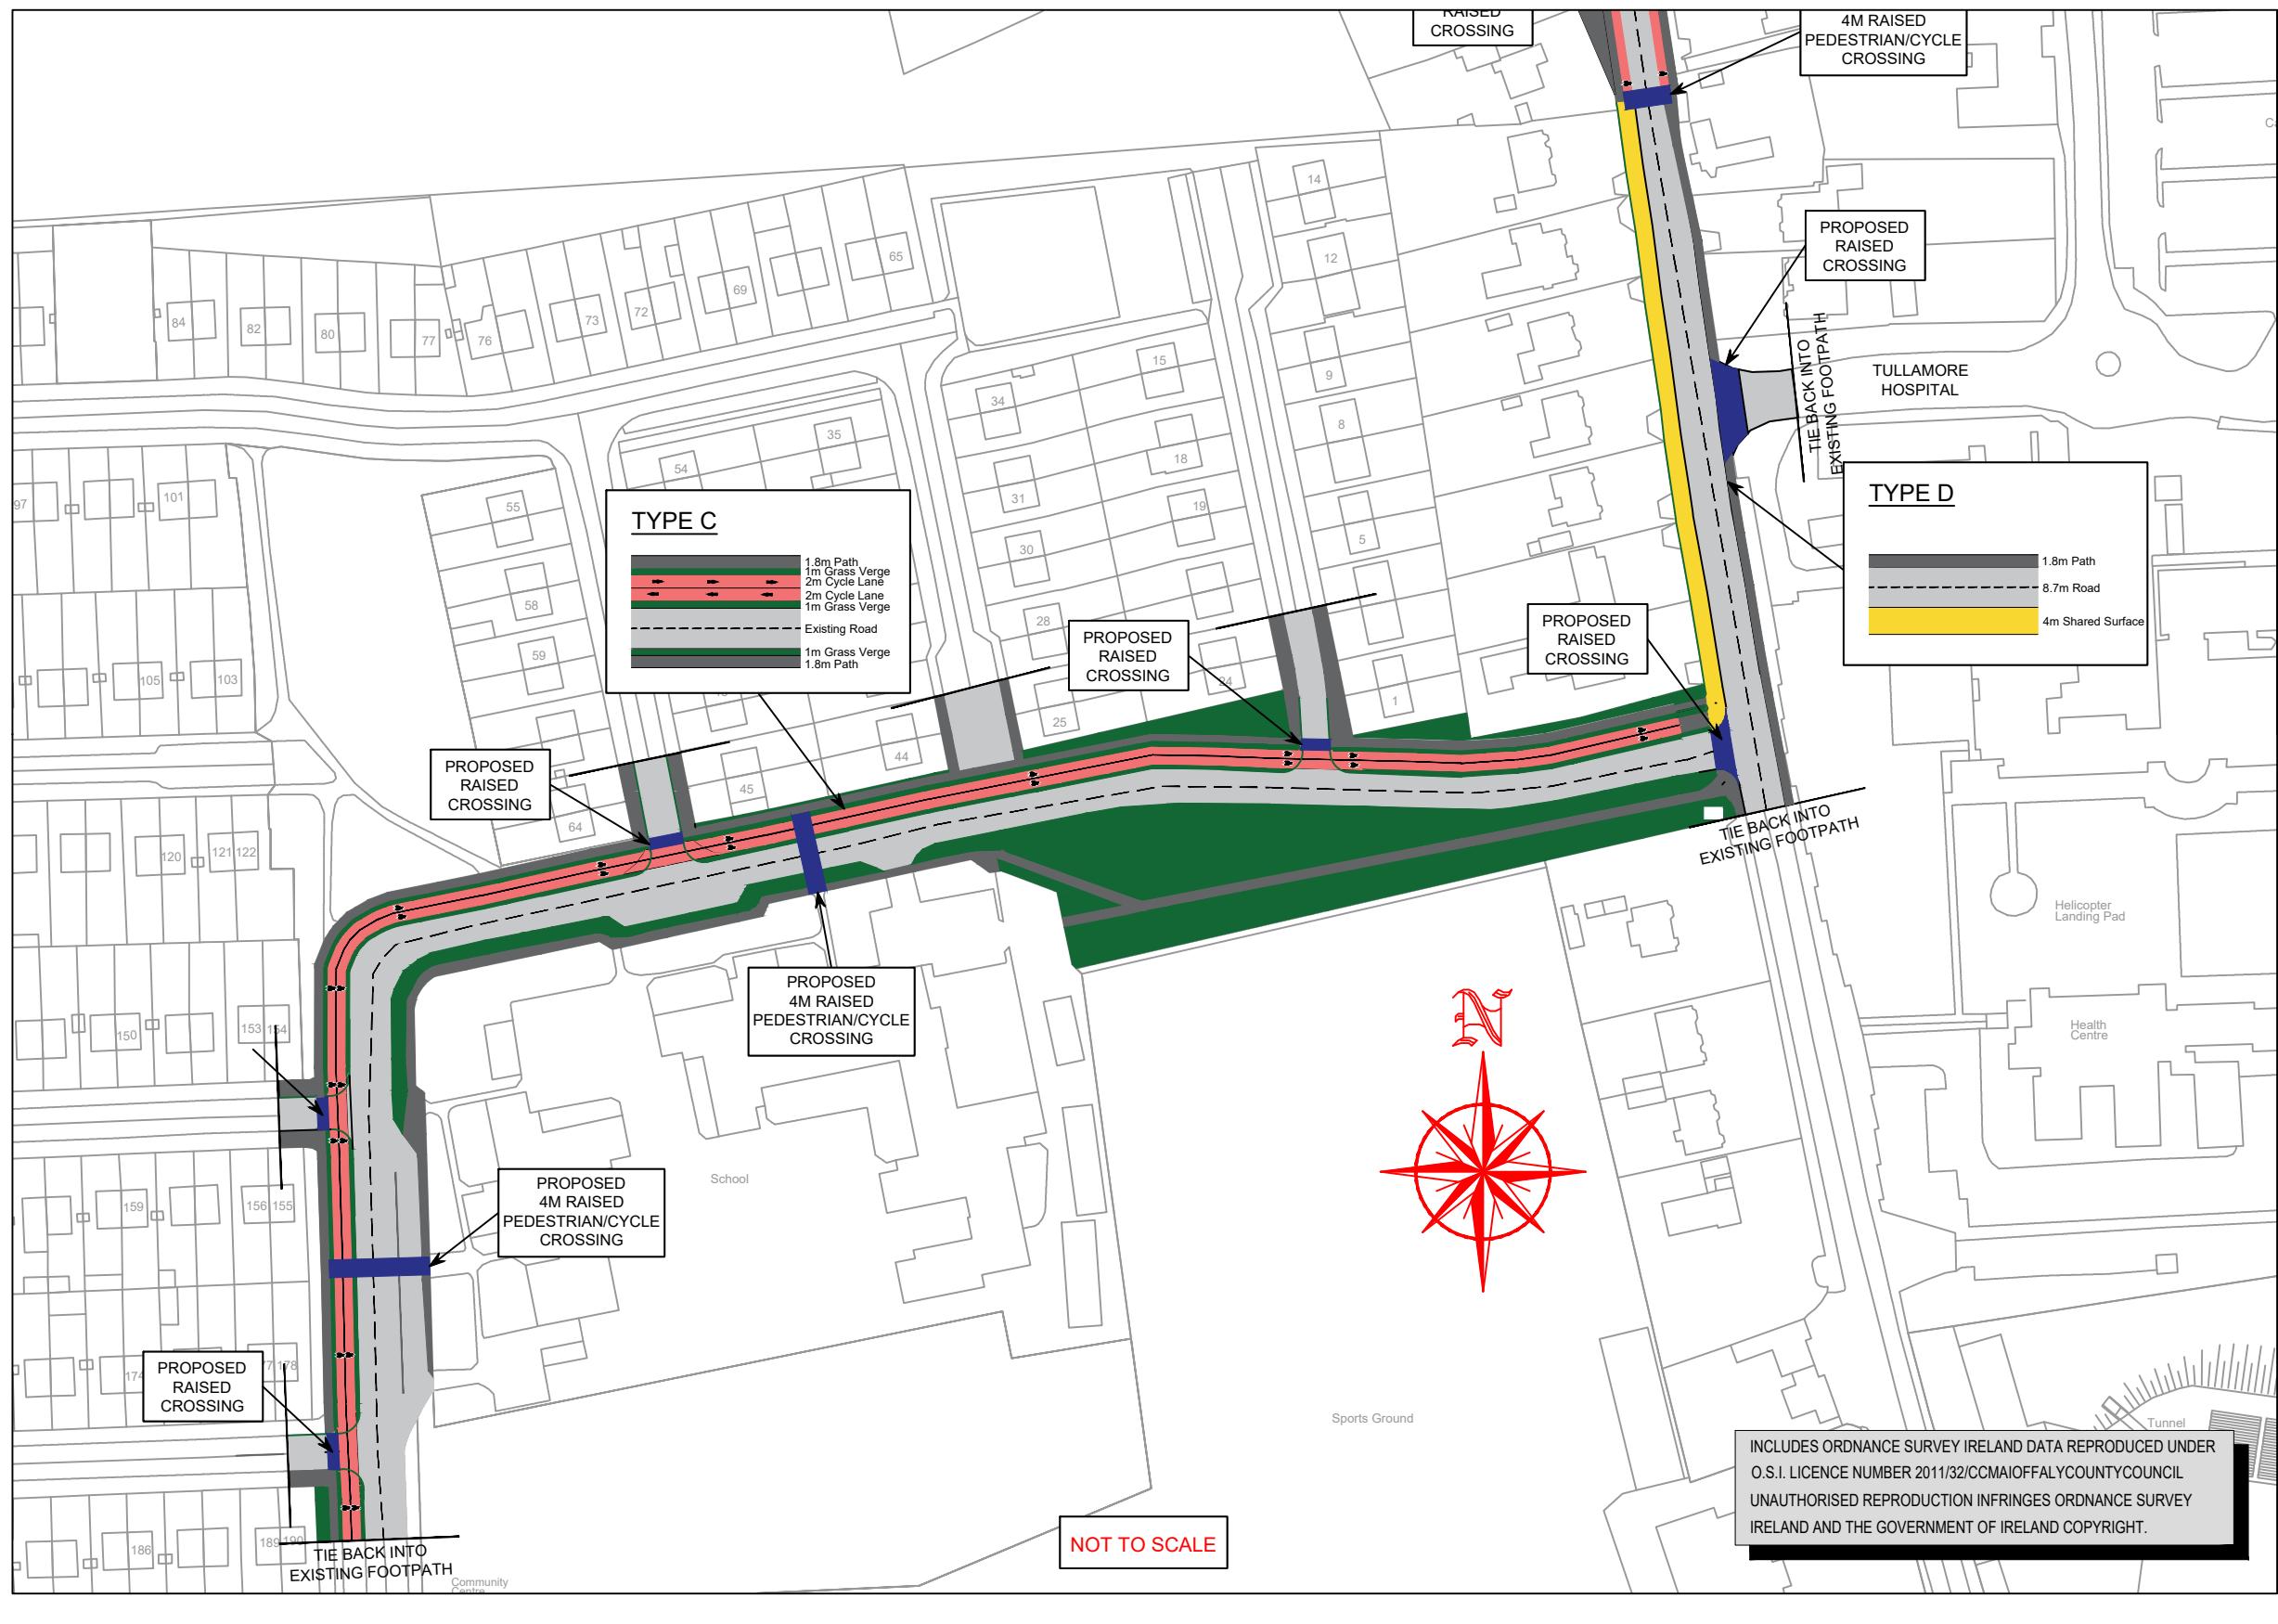


ALL WORKS TO COMPLY  
WITH THE NATIONAL  
CYCLE MANUAL & DMURS

**PRELIMINARY ISSUE**

Drawing Details			
Description	Date	Int.	Rev.
 Offaly County Council Tel. (057) 9346800			
Tom Shanahan, Director of Services Aras an Chontae, Charleville Rd., Tullamore.			
PROJECT	TULLAMORE CYCLE NETWORK PHASE 1		
TITLE	PROPOSED ARDEN VIEW/ARDEN ROAD LAYOUT		
SCALE	ROAD NO	PROJECT NO	DRAWING NO
AS SHOWN	N/A	TCN1	20 002
DATE	DRAWN BY	CHECKED	
SEPT 2020	T.R.	J.C.	

OFFALY COUNTY COUNCIL  
TULLAMORE CYCLE NETWORK PHASE 1  
PROPOSED ARDEN ROAD LAYOUT

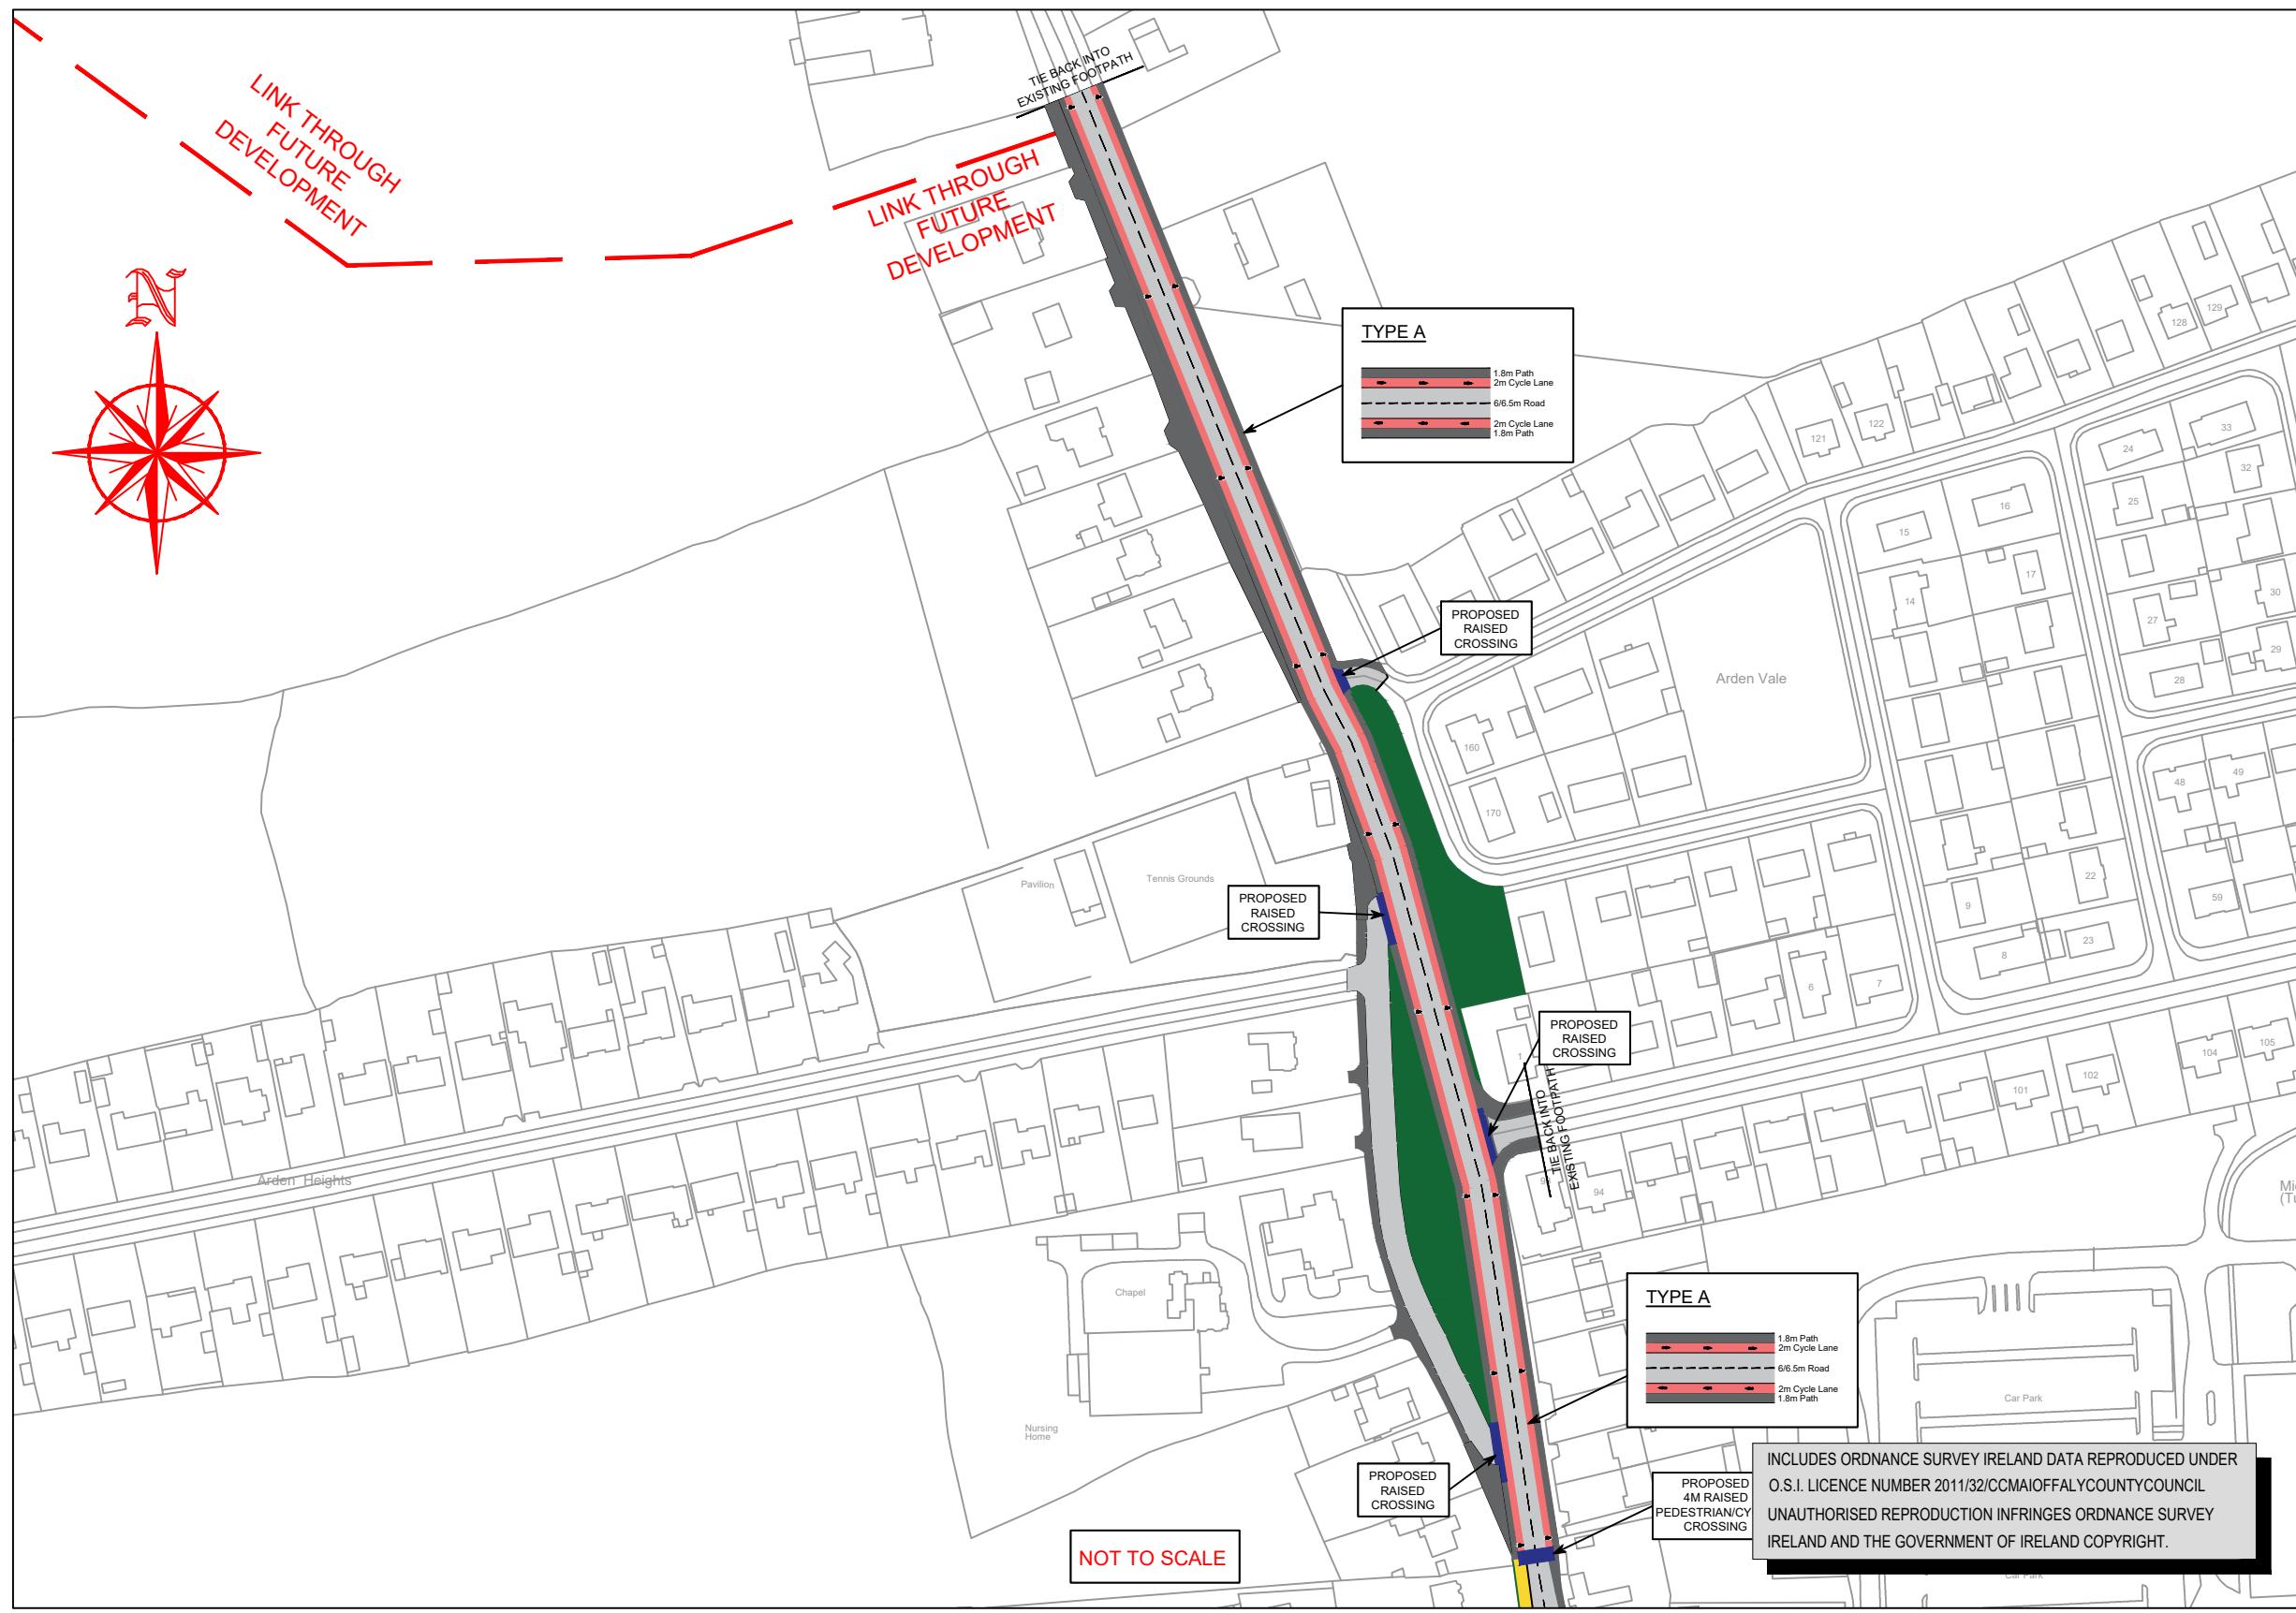


TAKEN FROM O.S. SHEET: 3371-22, 3371-23, 3434-02, 3434-03

ALL WORKS TO COMPLY  
WITH THE NATIONAL  
CYCLE MANUAL & DMURS

**PRELIMINARY ISSUE**

DESCRIPTION	DATE	INT.	REV
 Offaly County Council Tel. (057) 9346800			
Tom Shanahan, Director of Services Aras an Chontae, Charleville Rd., Tullamore.			
<b>PROJECT</b> TULLAMORE CYCLE NETWORK PHASE 1			
<b>TITLE</b> PROPOSED ARDEN ROAD LAYOUT			
<b>SCALE</b> AS SHOWN	ROAD NO N/A	PROJECT NO TCN1	DRAWING NO 20 003
	DATE SEPT 2020	DRAWN BY T.R.	CHECKED J.C.

OFFALY COUNTY COUNCIL  
TULLAMORE CYCLE NETWORK PHASE 1  
PROPOSED COLLINS LANE LAYOUT

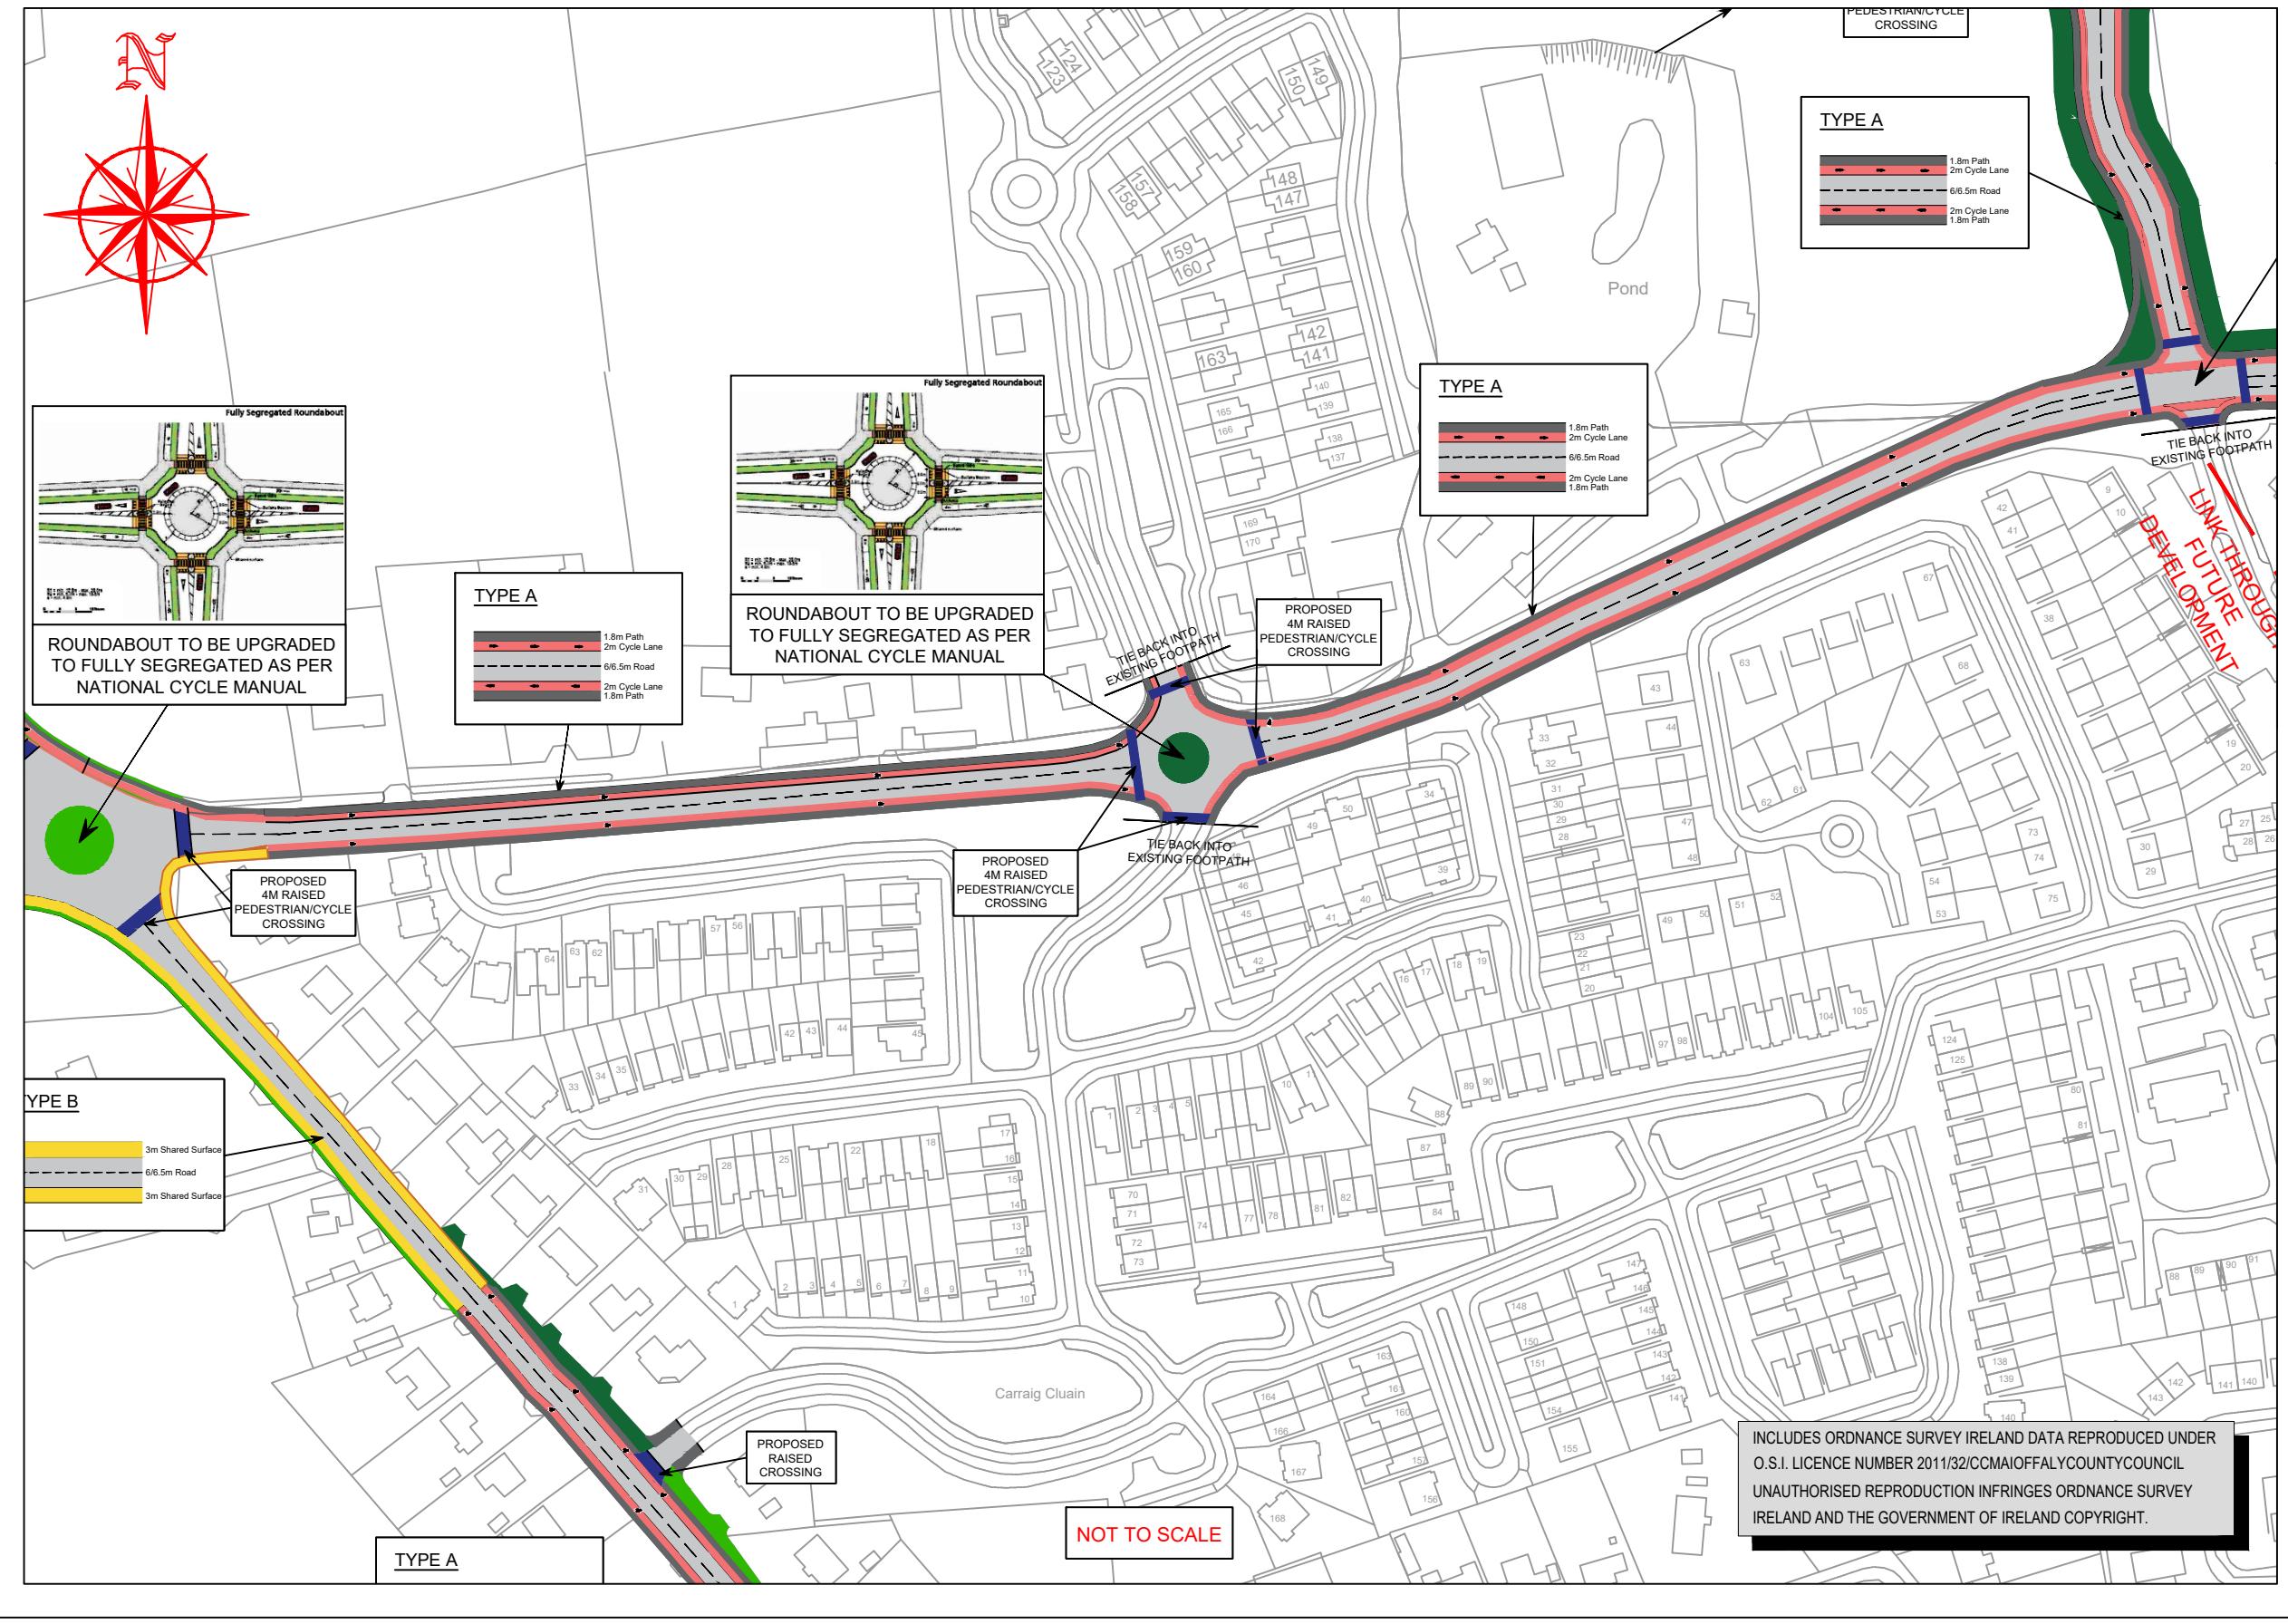


ALL WORKS TO COMPLY WITH THE NATIONAL CYCLE MANUAL & DMURS

**PRELIMINARY ISSUE**

DESCRIPTION	DATE	INT.	REV
Offaly County Council			
Tom Shanahan, Director of Services Aras an Chontae, Charleville Rd., Tullamore.			
PROJECT	TULLAMORE CYCLE NETWORK PHASE 1		
TITLE	PROPOSED COLLINS LANE LAYOUT		
SCALE AS SHOWN	ROAD NO N/A	PROJECT NO TCN1	DRAWING NO 20 004
	DATE SEPT 2020	DRAWN BY T.R.	CHECKED J.C.

OFFALY COUNTY COUNCIL  
TULLAMORE CYCLE NETWORK PHASE 1  
PROPOSED CLARA ROAD LAYOUT

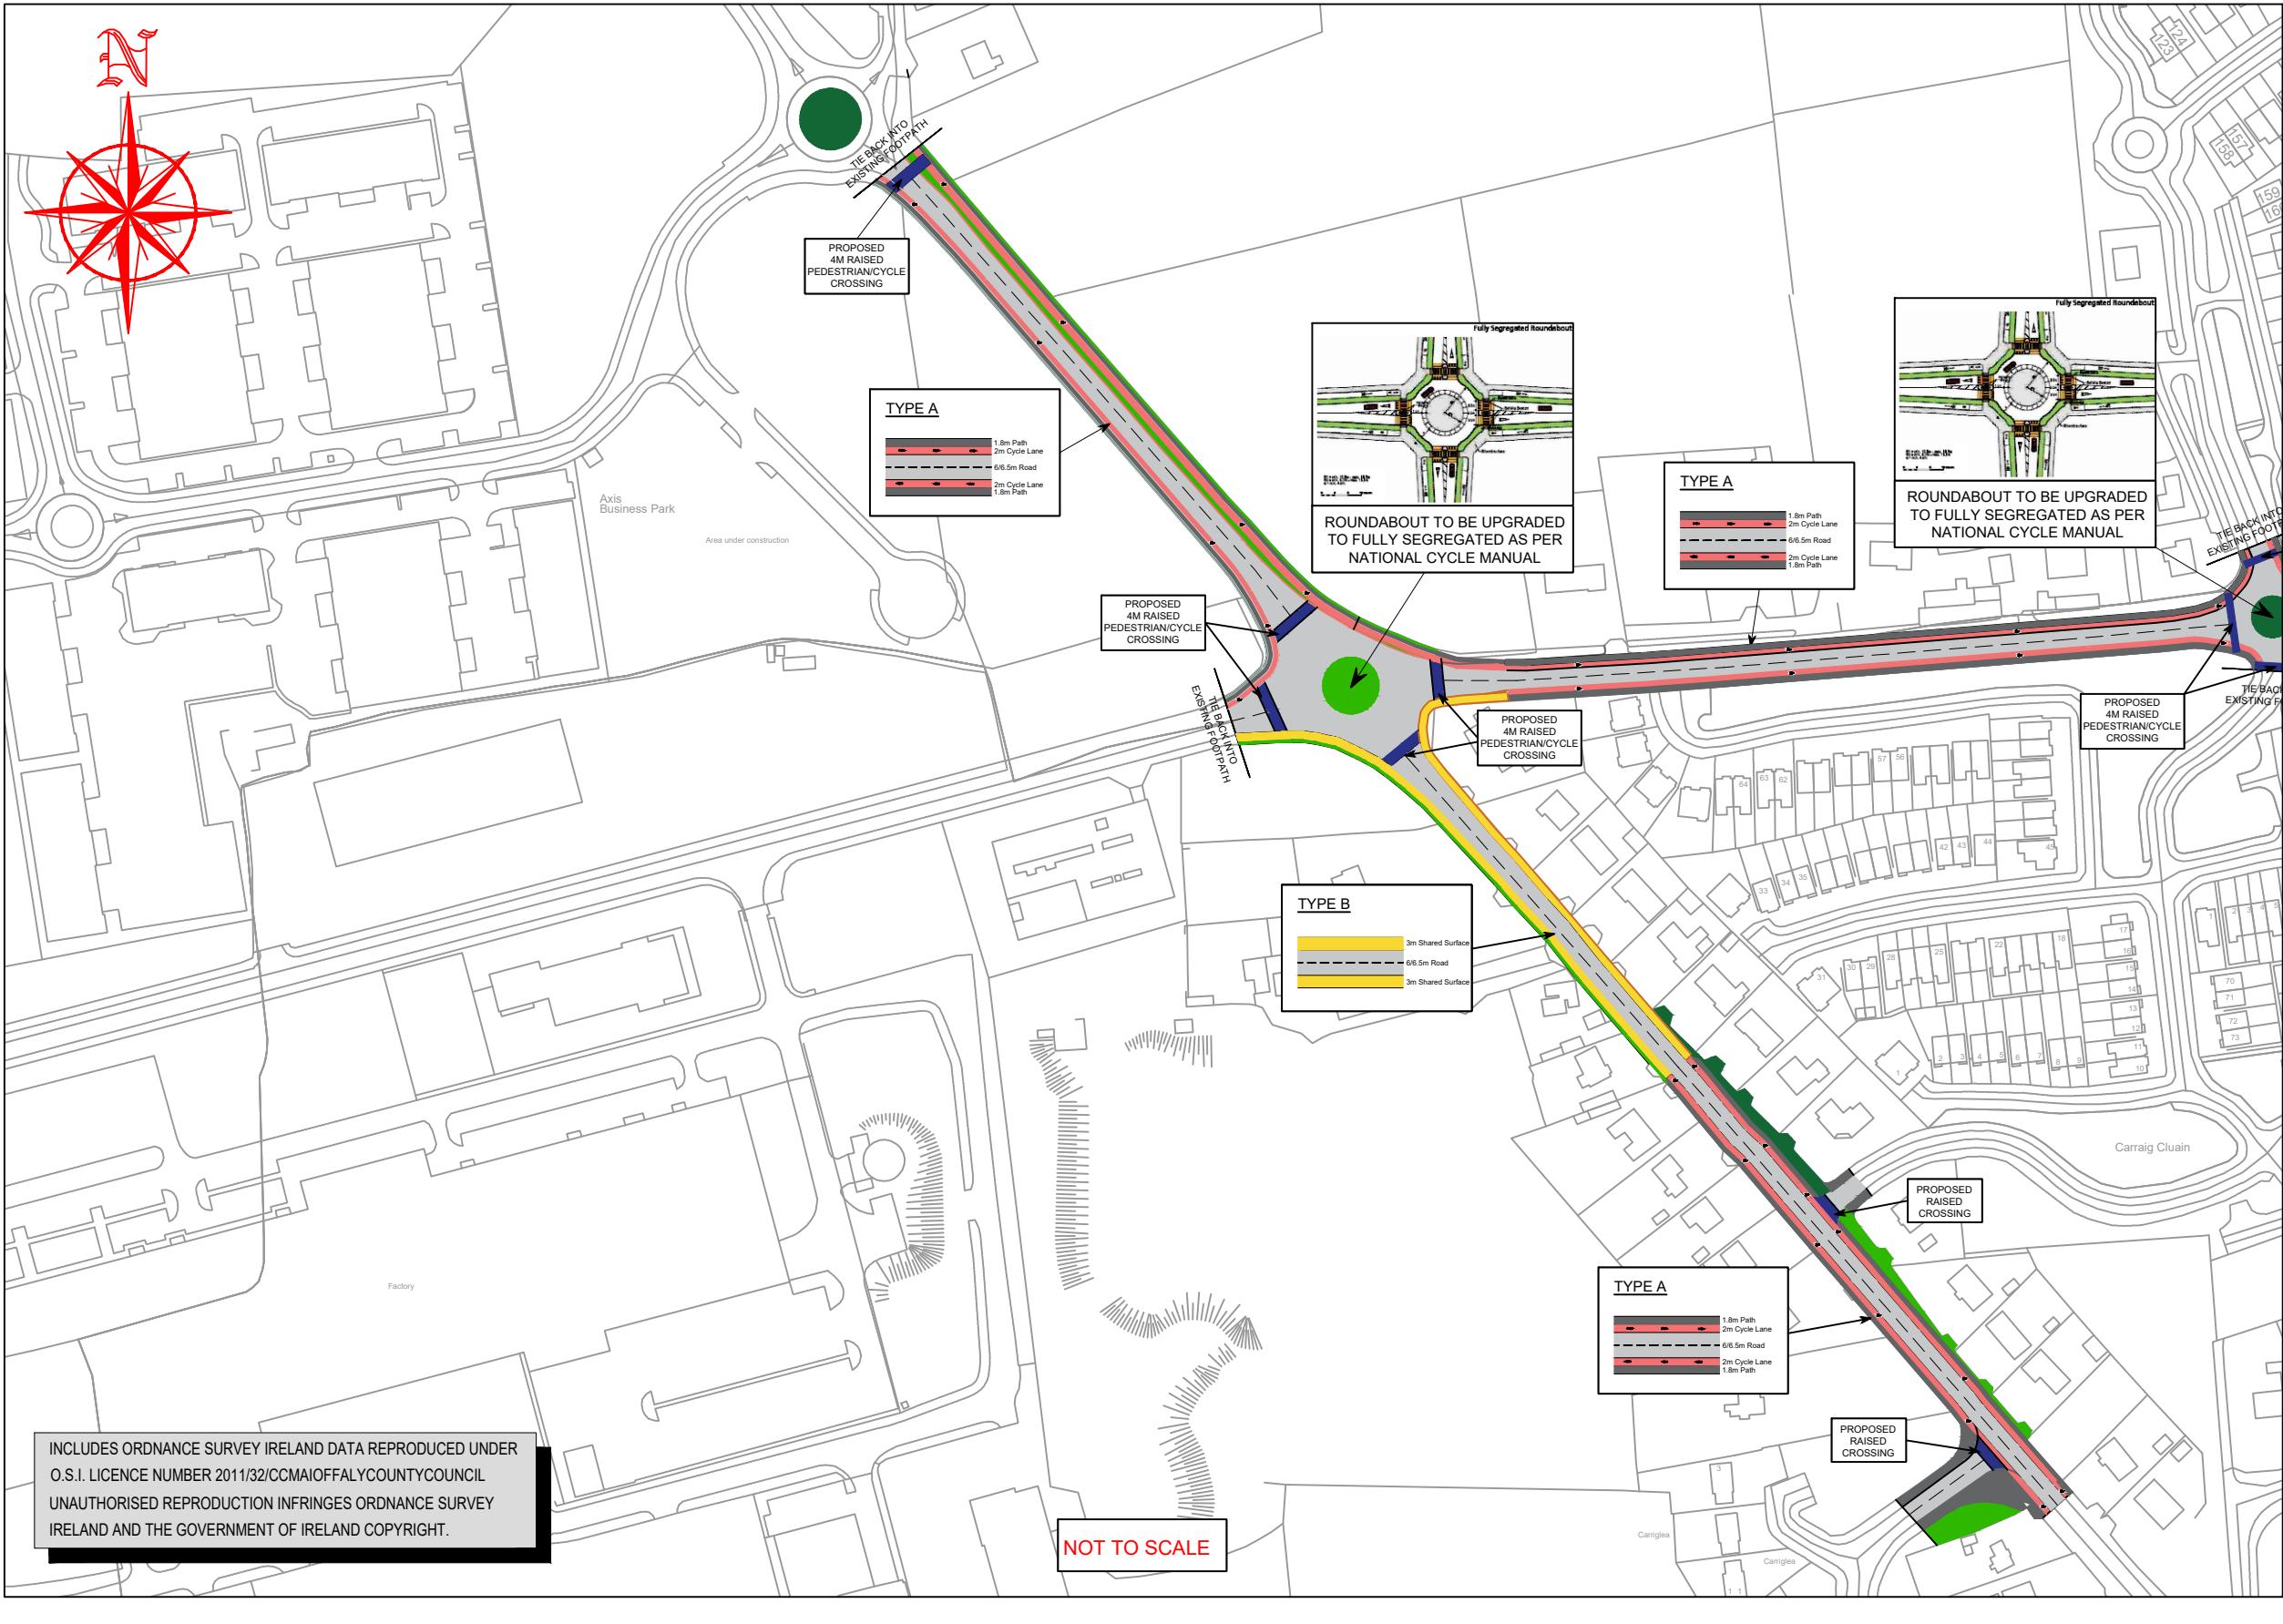


ALL WORKS TO COMPLY  
WITH THE NATIONAL  
CYCLE MANUAL & DMURS

**PRELIMINARY ISSUE**

DESCRIPTION	DATE	INT.	REV.
Offaly County Council			
Tom Shanahan, Director of Services Aras an Chontae, Charleville Rd., Tullamore.			
PROJECT	TULLAMORE CYCLE NETWORK PHASE 1		
TITLE	PROPOSED CLARA ROAD LAYOUT		
SCALE AS SHOWN	ROAD NO N/A	PROJECT NO TCN1	DRAWING NO 20 005
DATE SEPT 2020	DRAWN BY T.R.	CHECKED J.C.	

OFFALY COUNTY COUNCIL  
TULLAMORE CYCLE NETWORK PHASE 1  
PROPOSED COLLINS LANE TO SCHOOL LAYOUT

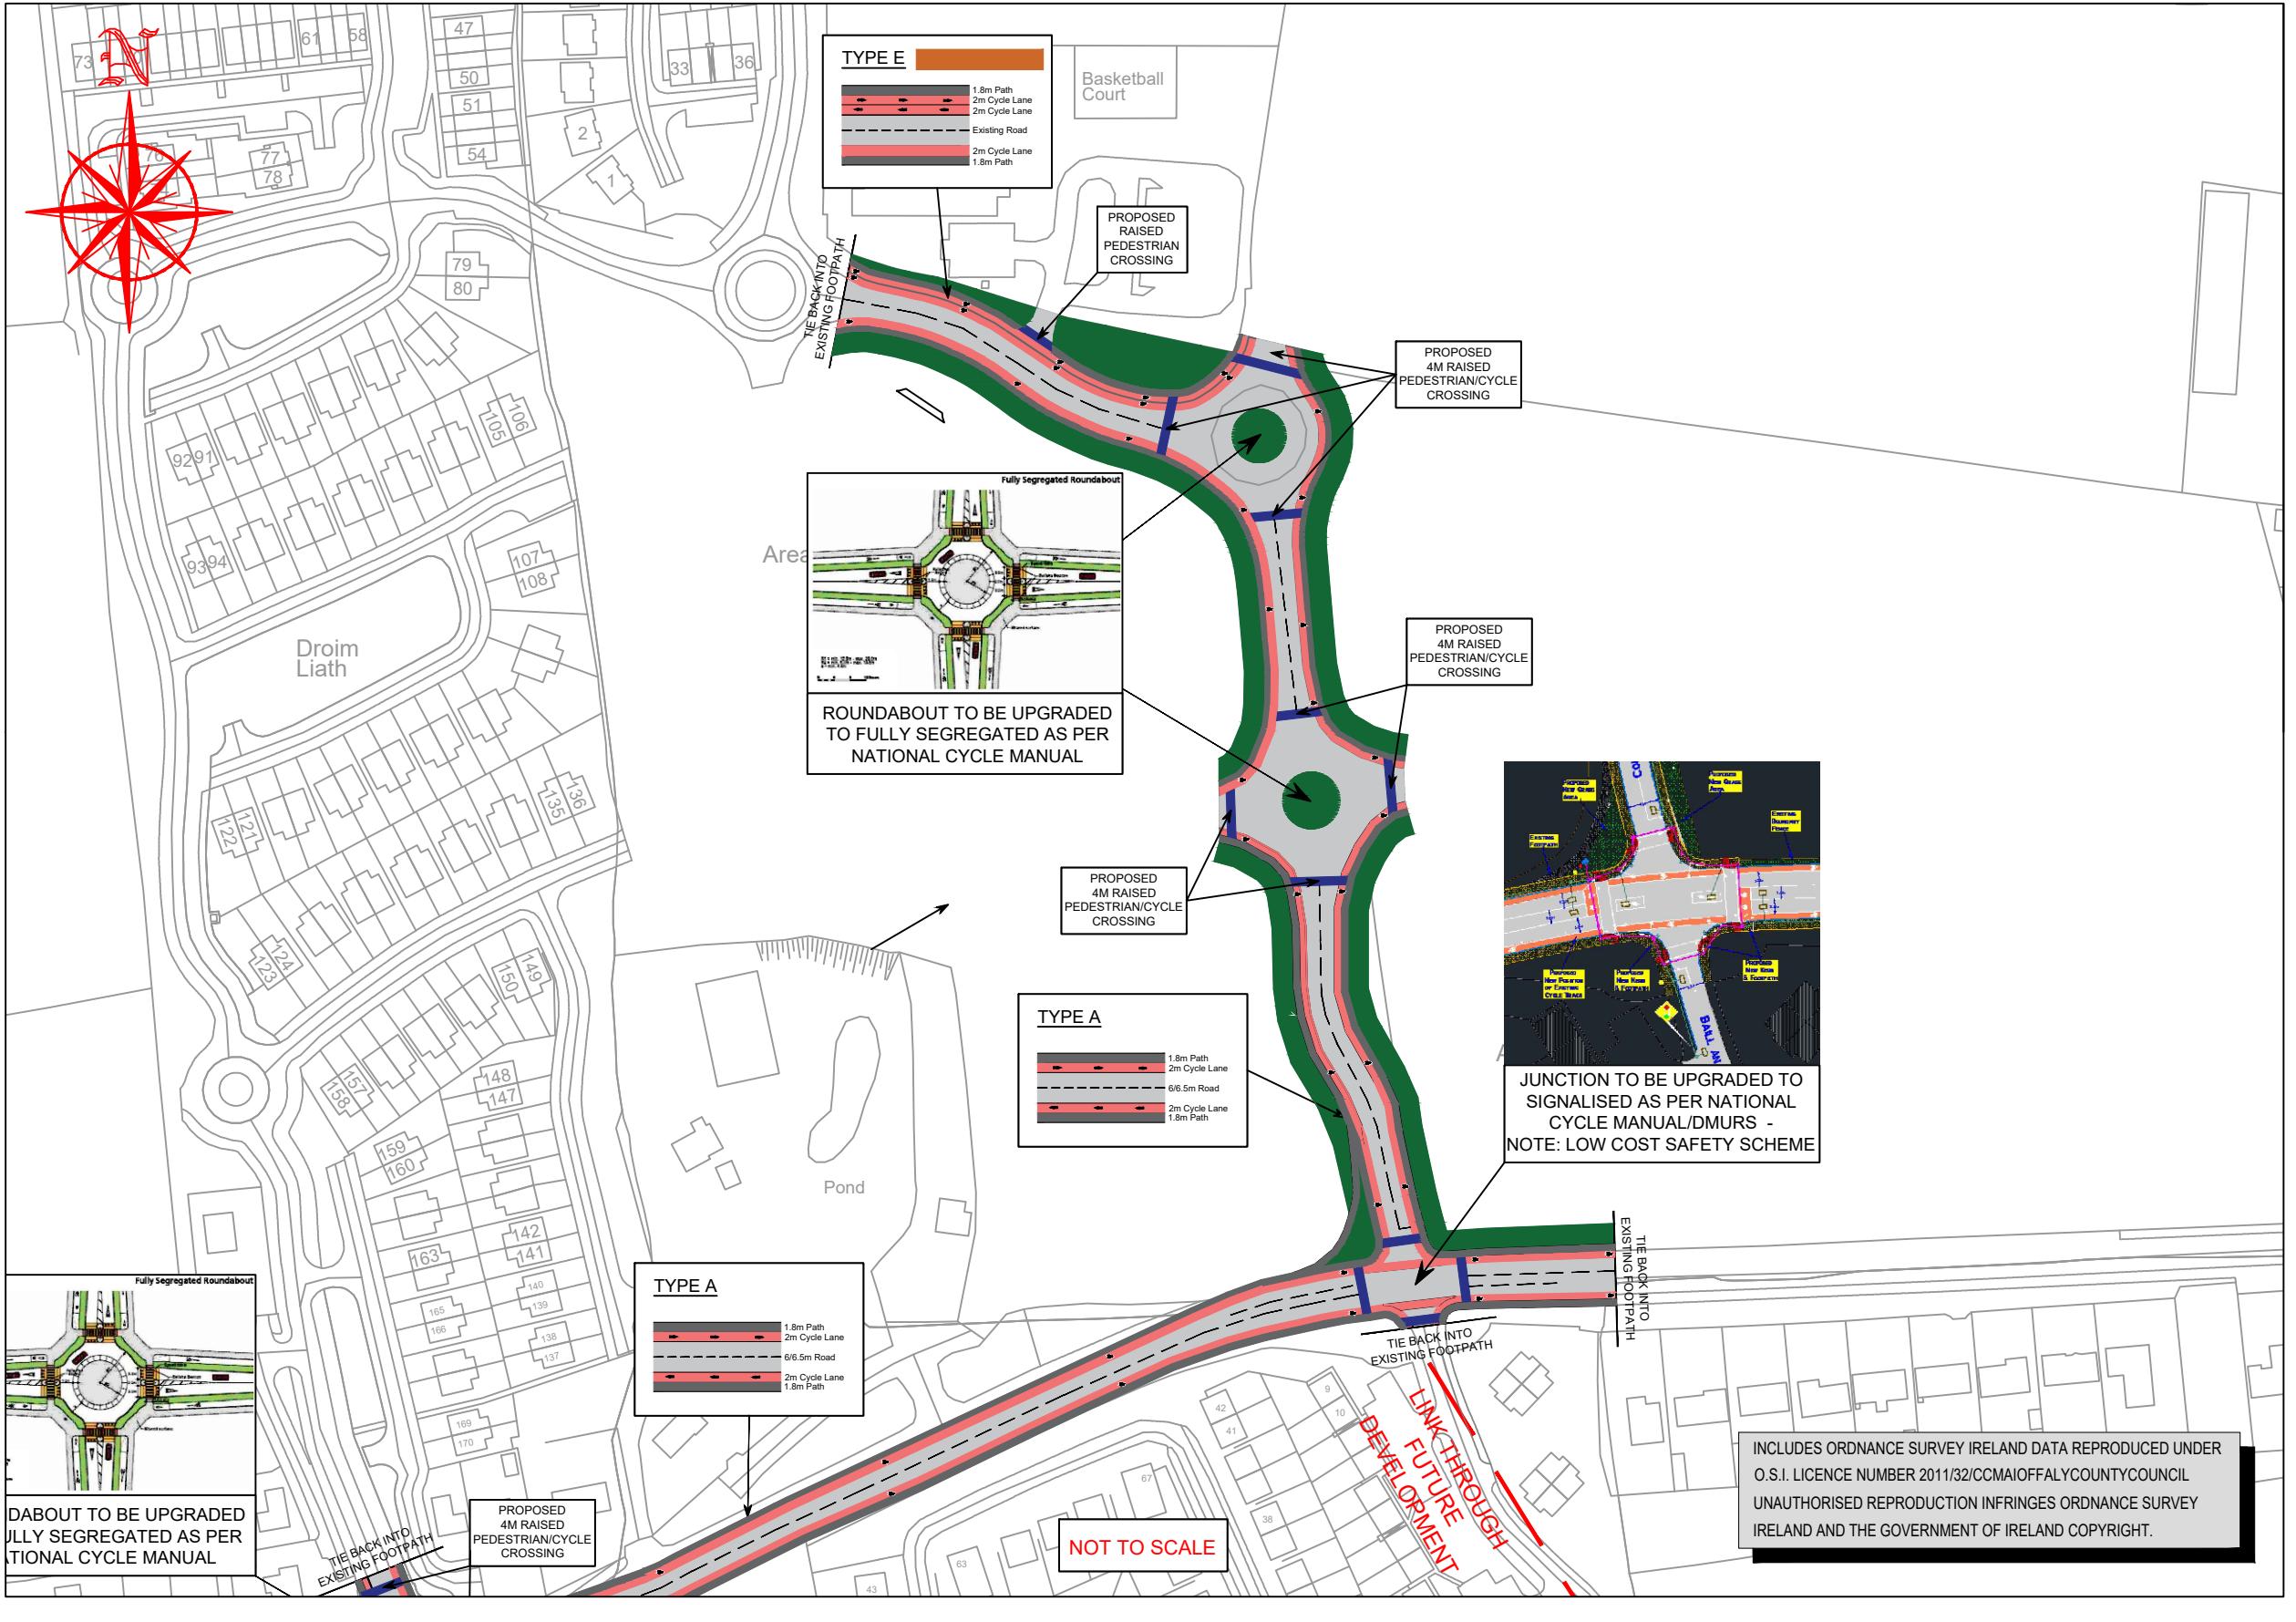


TAKEN FROM O.S. SHEET: 3371-22, 3371-C

ALL WORKS TO COMPLY  
WITH THE NATIONAL  
CYCLE MANUAL & DMURS

**PRELIMINARY ISSUE**

DESCRIPTION	DATE	INT.	REV
<b>Offaly County Council</b> Tel. (057) 9346800			
Tom Shanahan, Director of Services Aras an Chontae, Charleville Rd., Tullamore.			
<b>PROJECT</b> TULLAMORE CYCLE NETWORK PHASE PHASE 1			
<b>TITLE</b> PROPOSED COLLINS LANE TO SCHOOL LAYOUT			
SCALE AS SHOWN	ROAD NO N/A	PROJECT NO TCN1	DRAWING NO 20 006
DATE SEPT 2020	DRAWN BY T.R.	CHECKED J.C.	

OFFALY COUNTY COUNCIL  
TULLAMORE CYCLE NETWORK PHASE 1  
CYCLE LANE CONSTRUCTION DETAIL

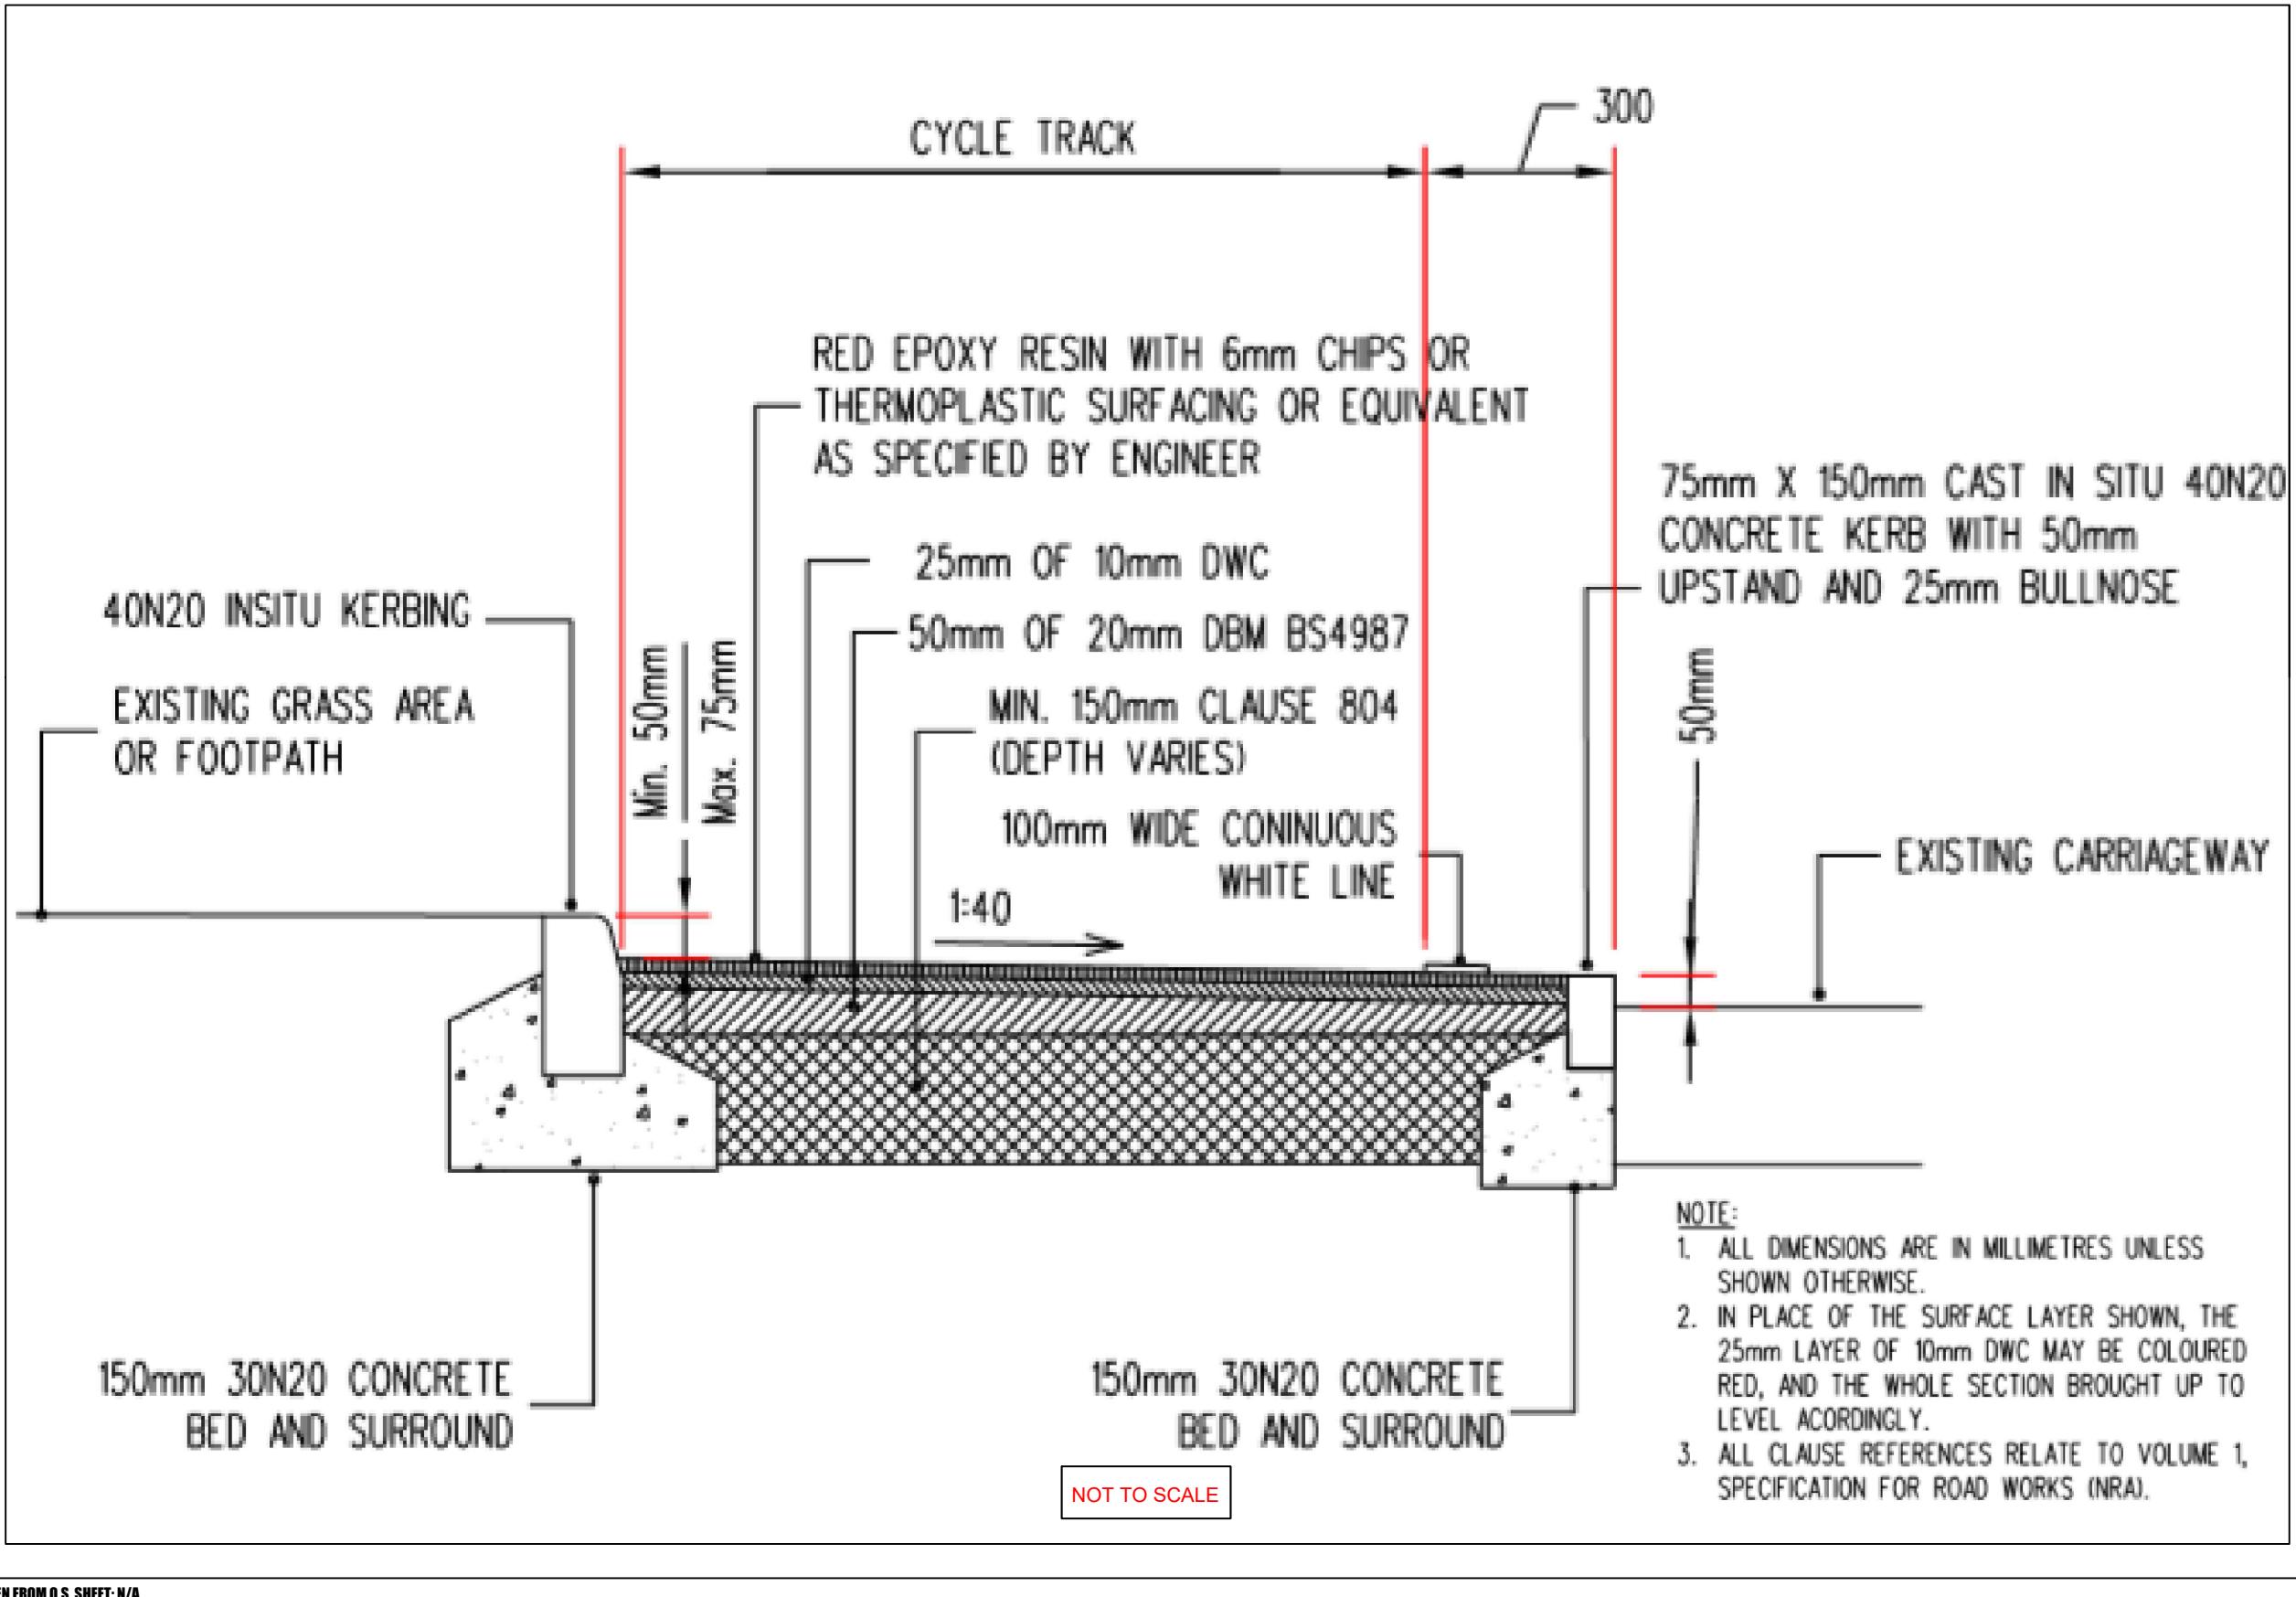

NOTE: CONSTRUCTION DETAIL IS TAKEN FROM THE NATIONAL CYCLE MANUAL - PAGE 192

ALL WORKS TO COMPLY WITH THE NATIONAL CYCLE MANUAL & DMURS

**PRELIMINARY ISSUE**

DESCRIPTION	DATE	INT.	REV
 Offaly County Council Tel: (057) 9346800			
Tom Shanahan, Director of Services Aras an Chontae, Charleville Rd., Tullamore.			
PROJECT TULLAMORE CYCLE NETWORK PHASE 1			
TITLE CYCLE LANE CONSTRUCTION DETAIL			
SCALE AS SHOWN	ROAD NO N/A	PROJECT NO TCN1	DRAWING NO 20 007
	DATE SEPT 2020	DRAWN BY T.R.	CHECKED J.C.